


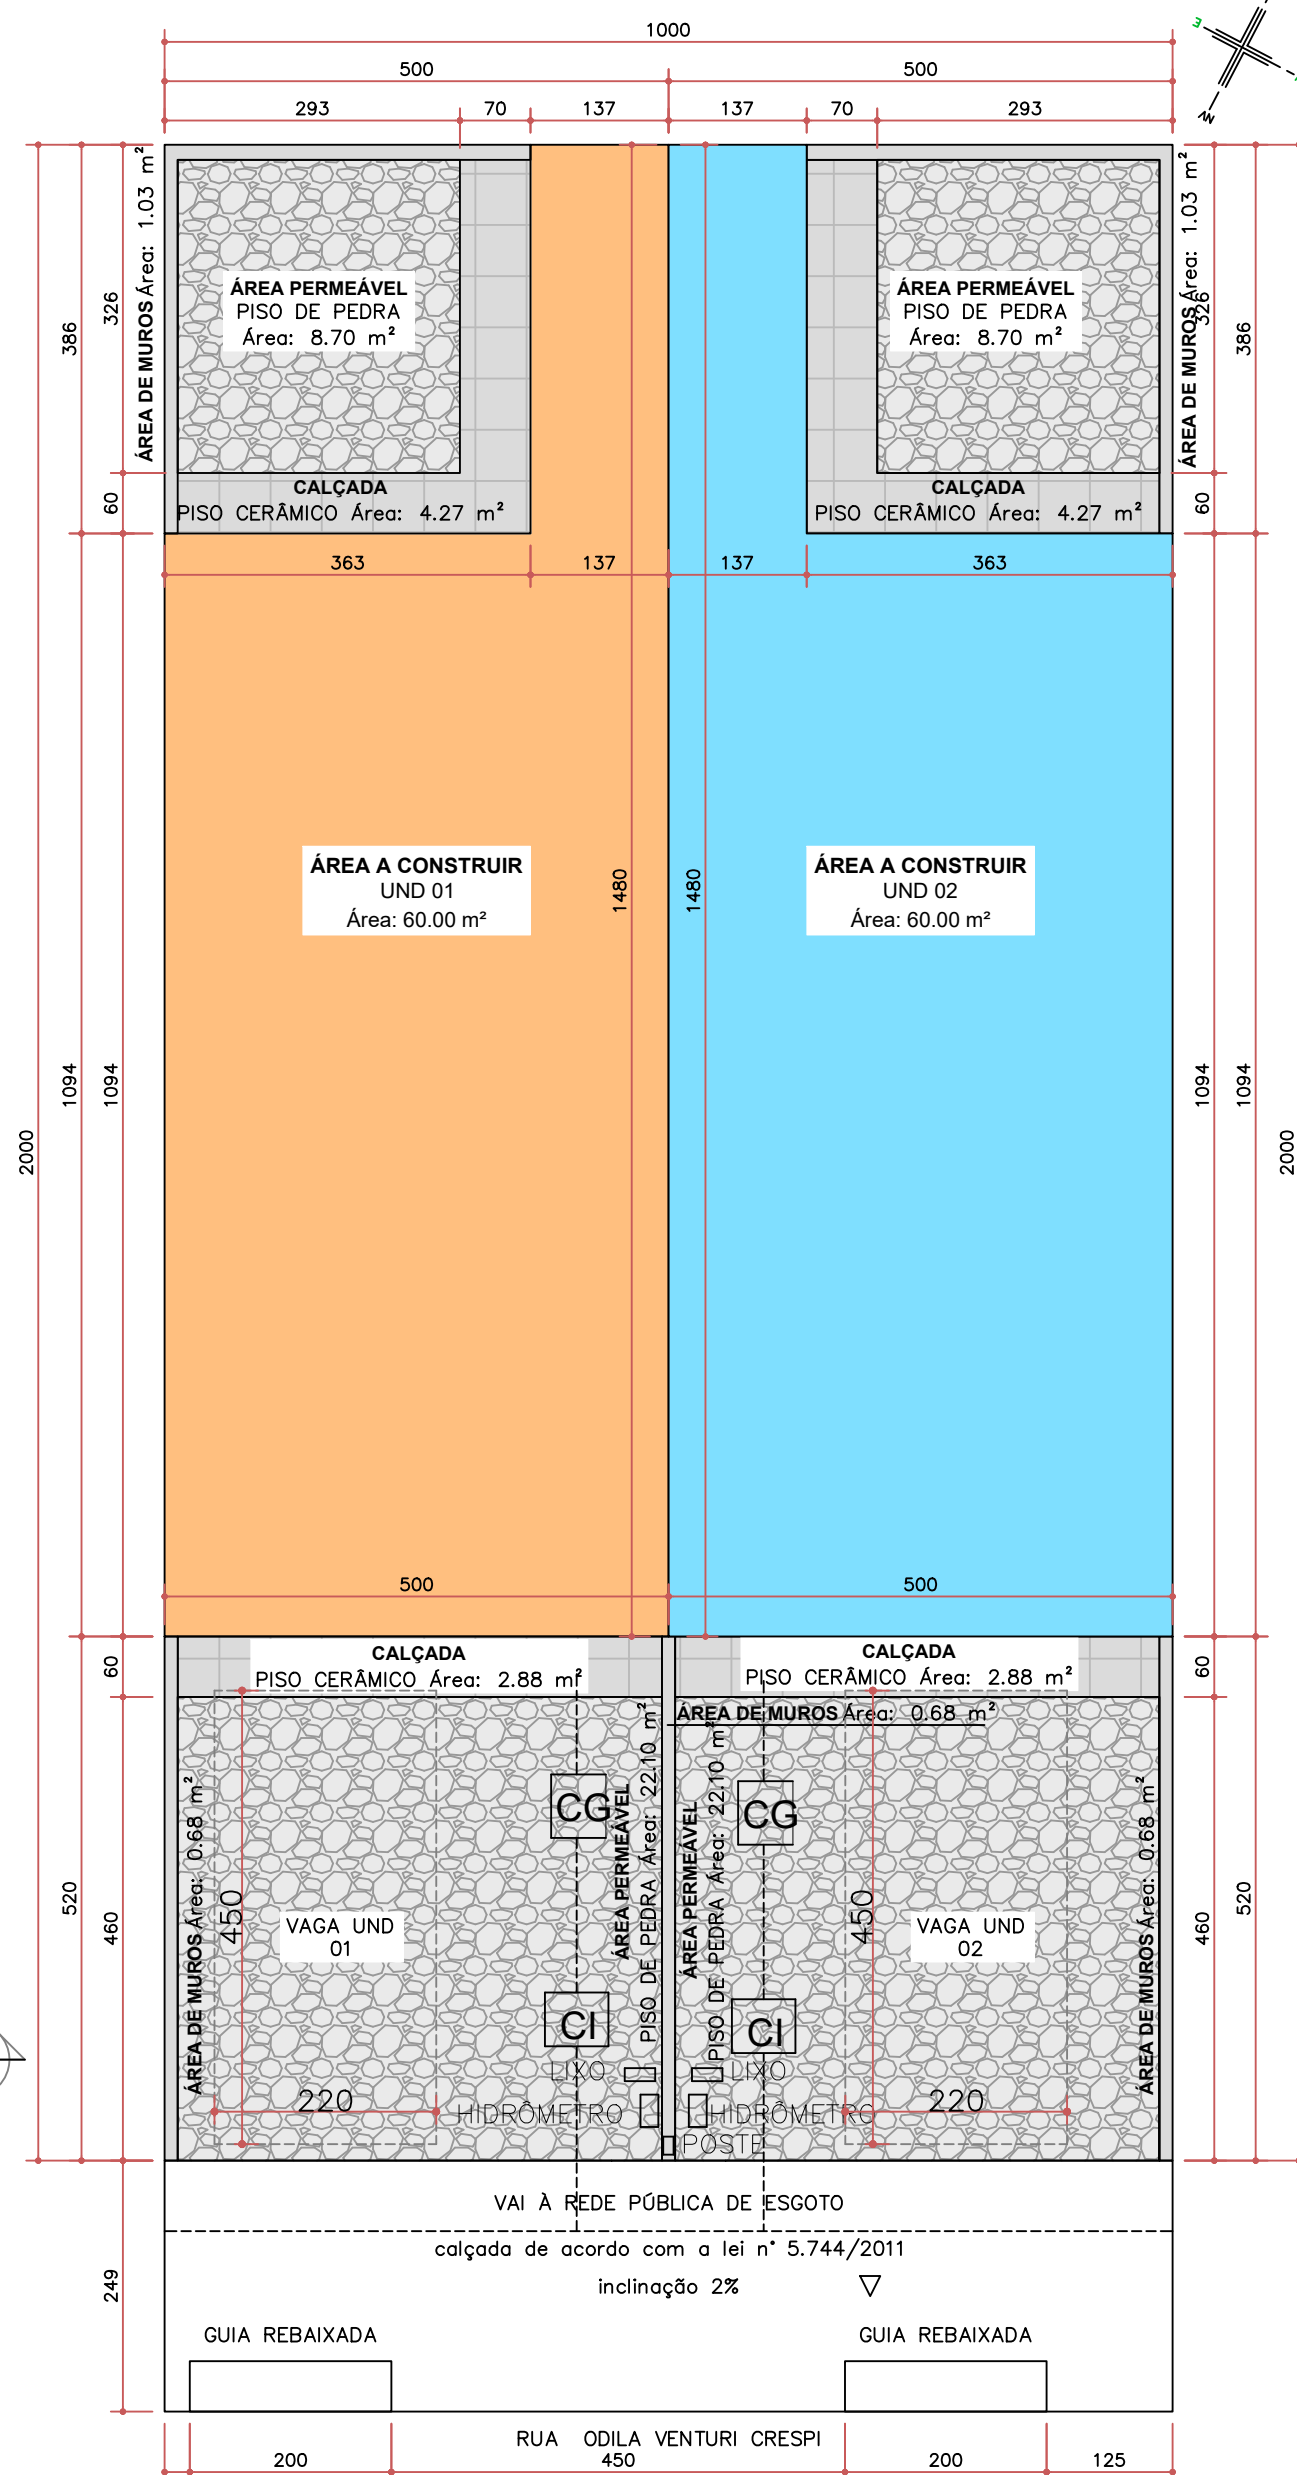


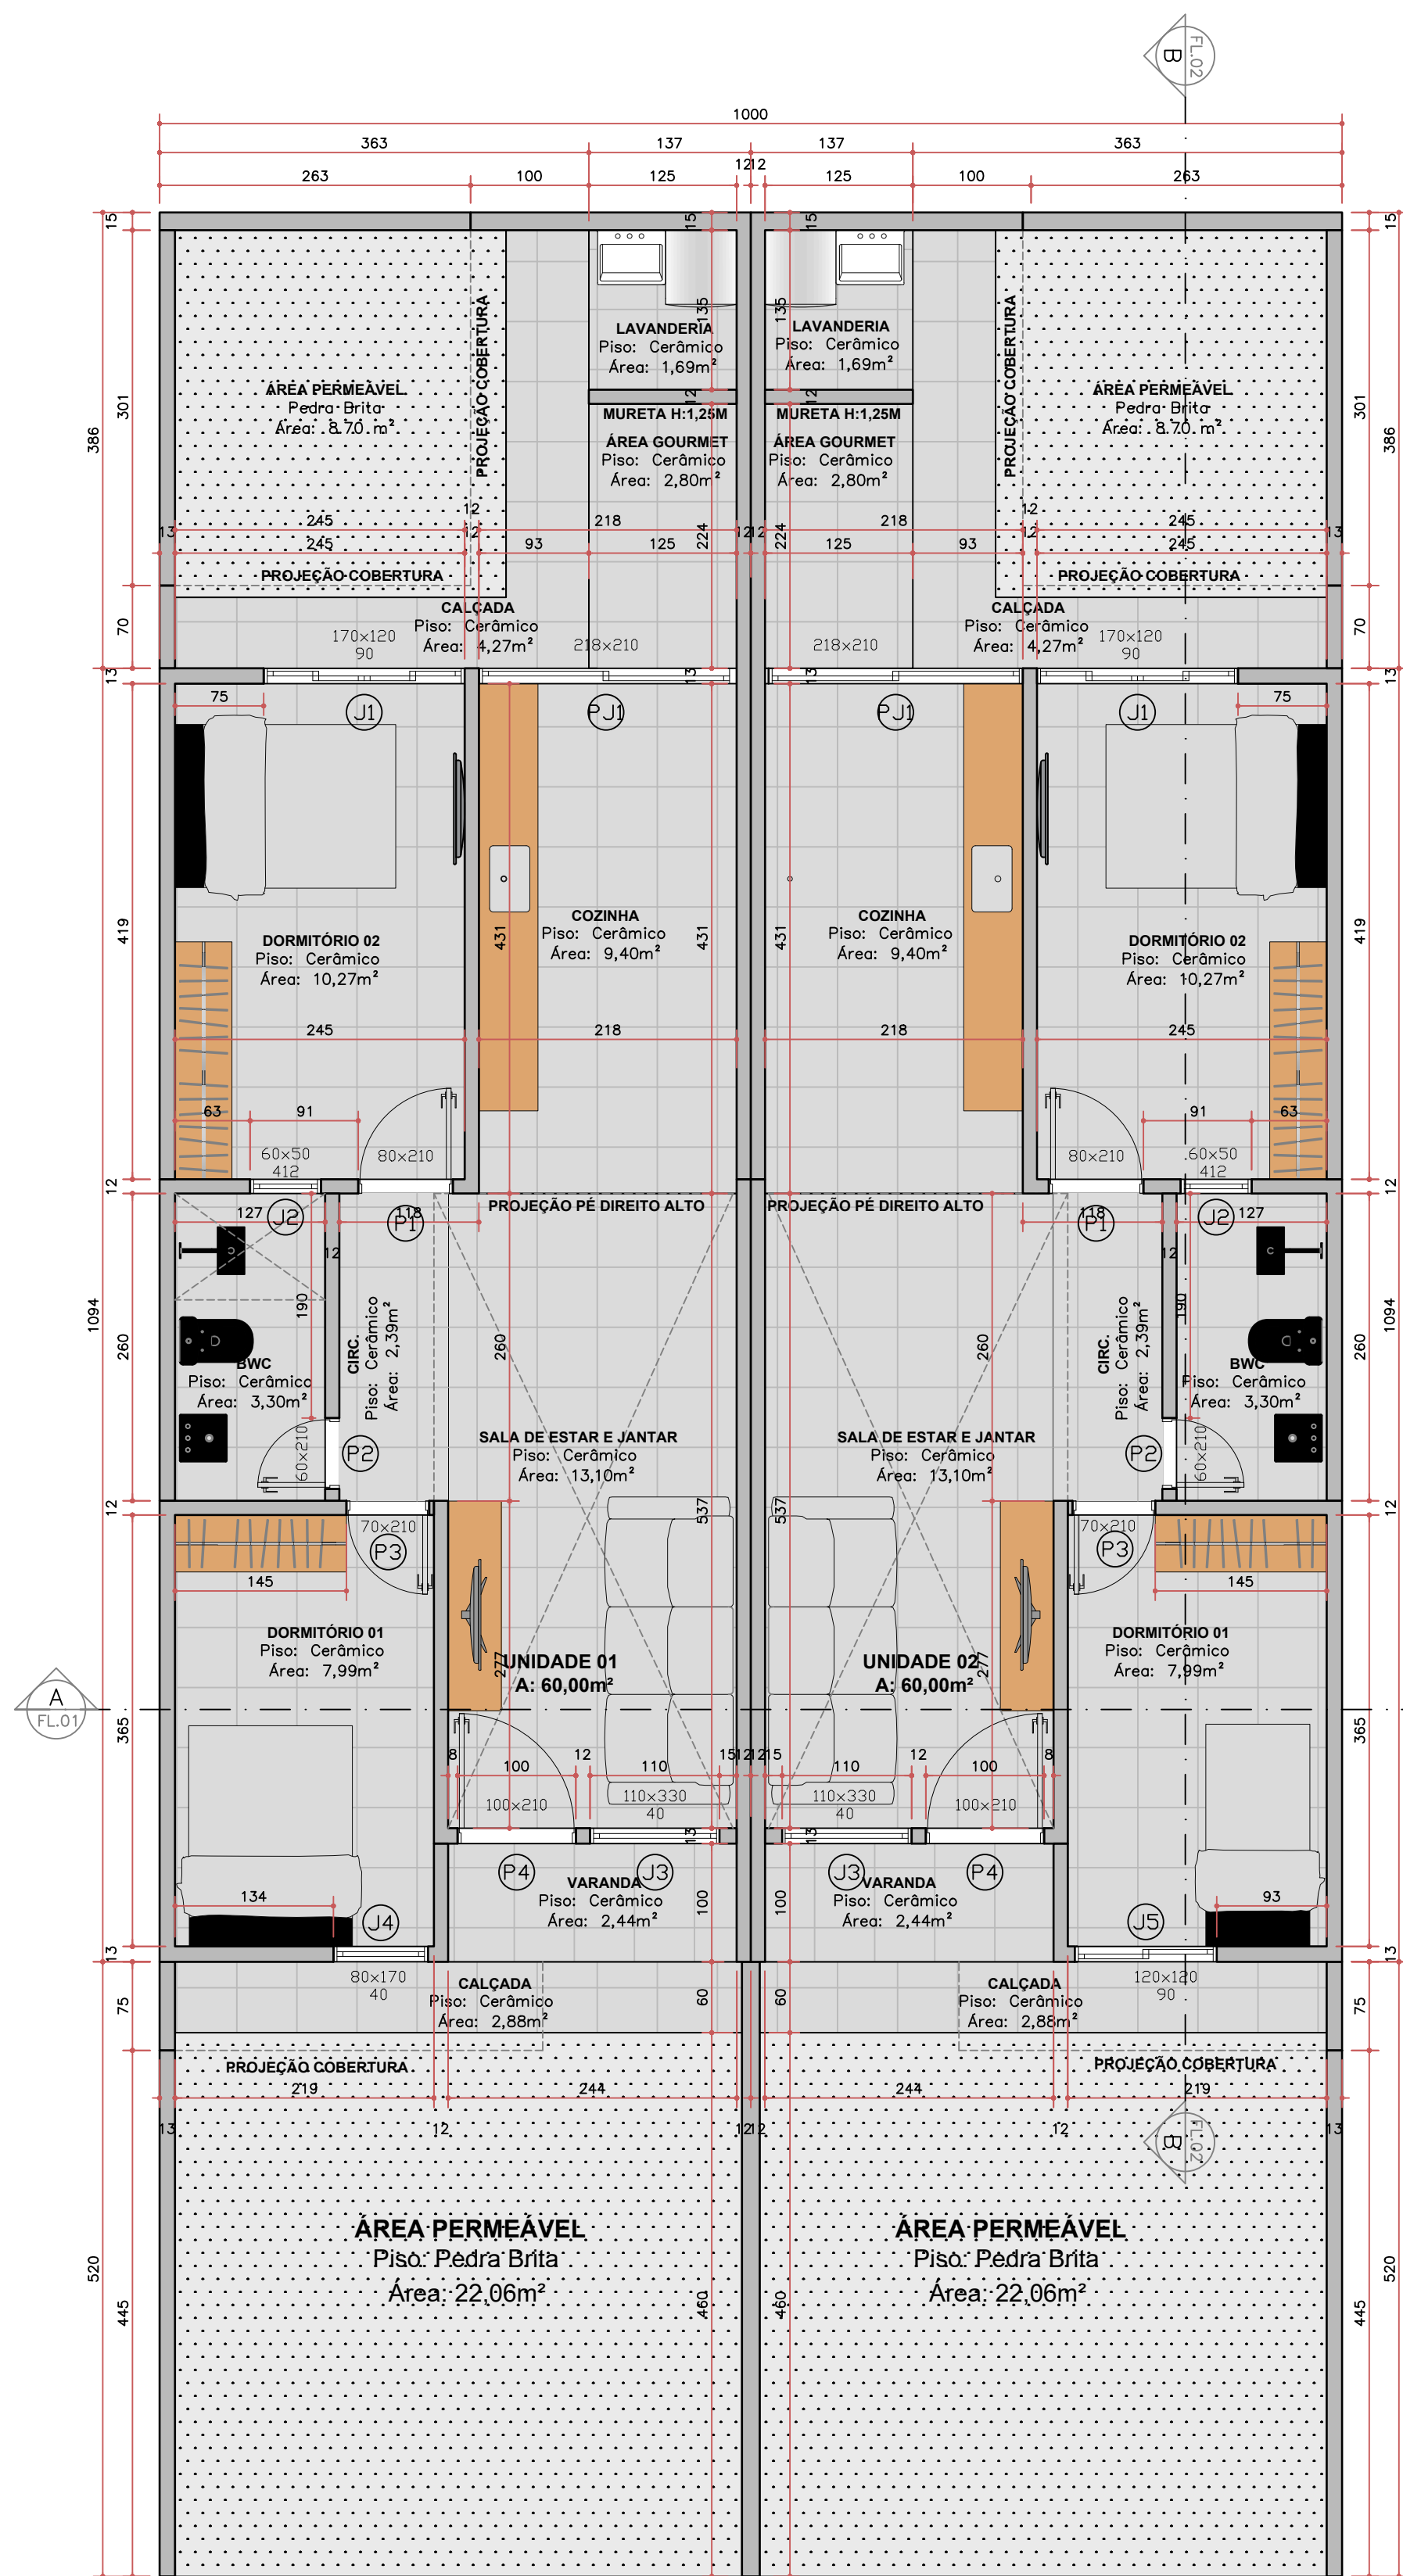


SITUAÇÃO
ESCALA: 1/75

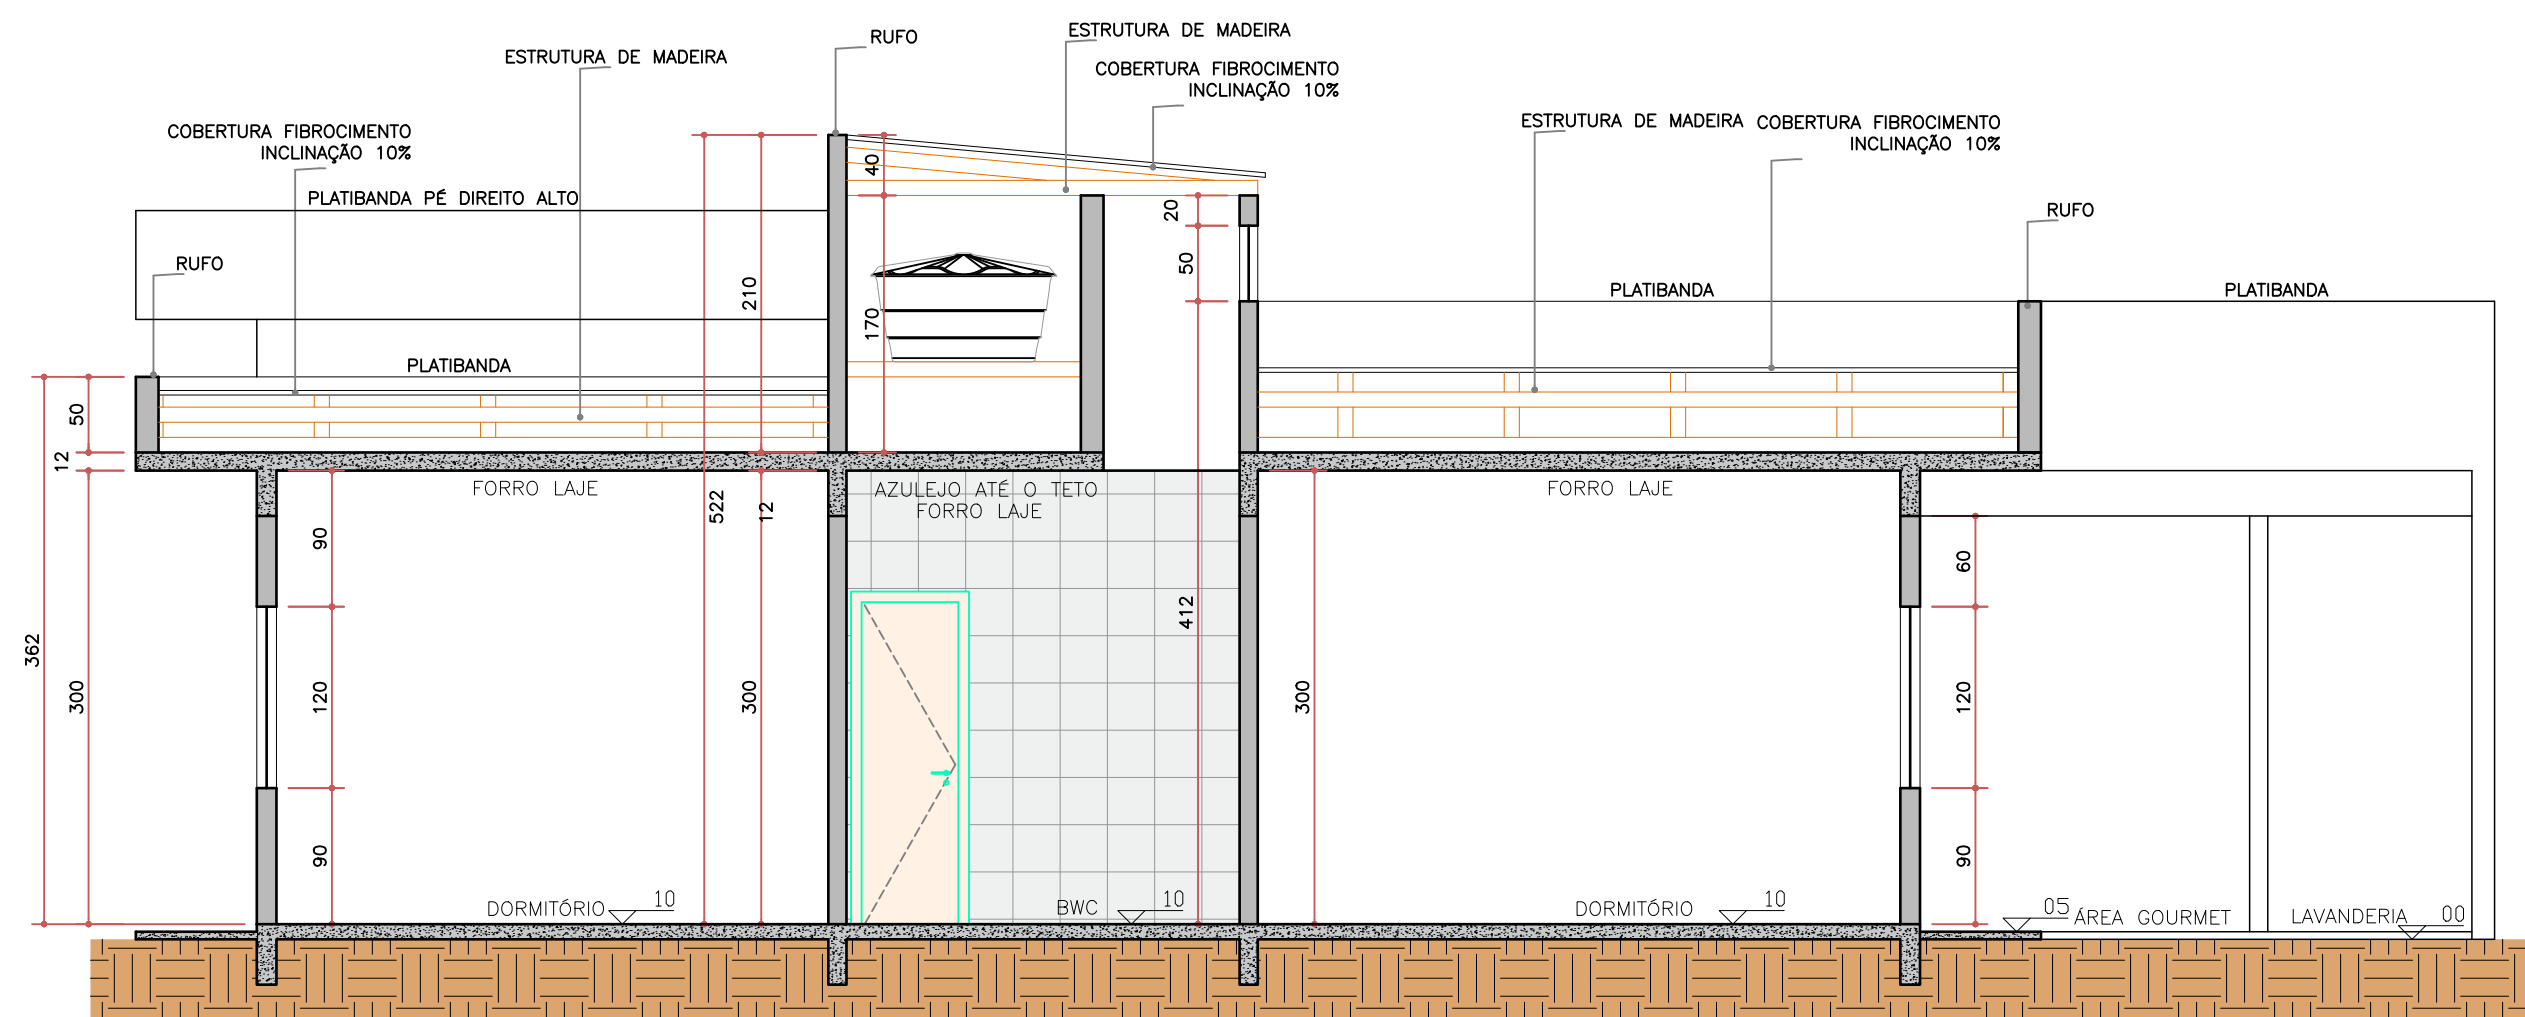


CORTE B1
ESCALA: 1/50

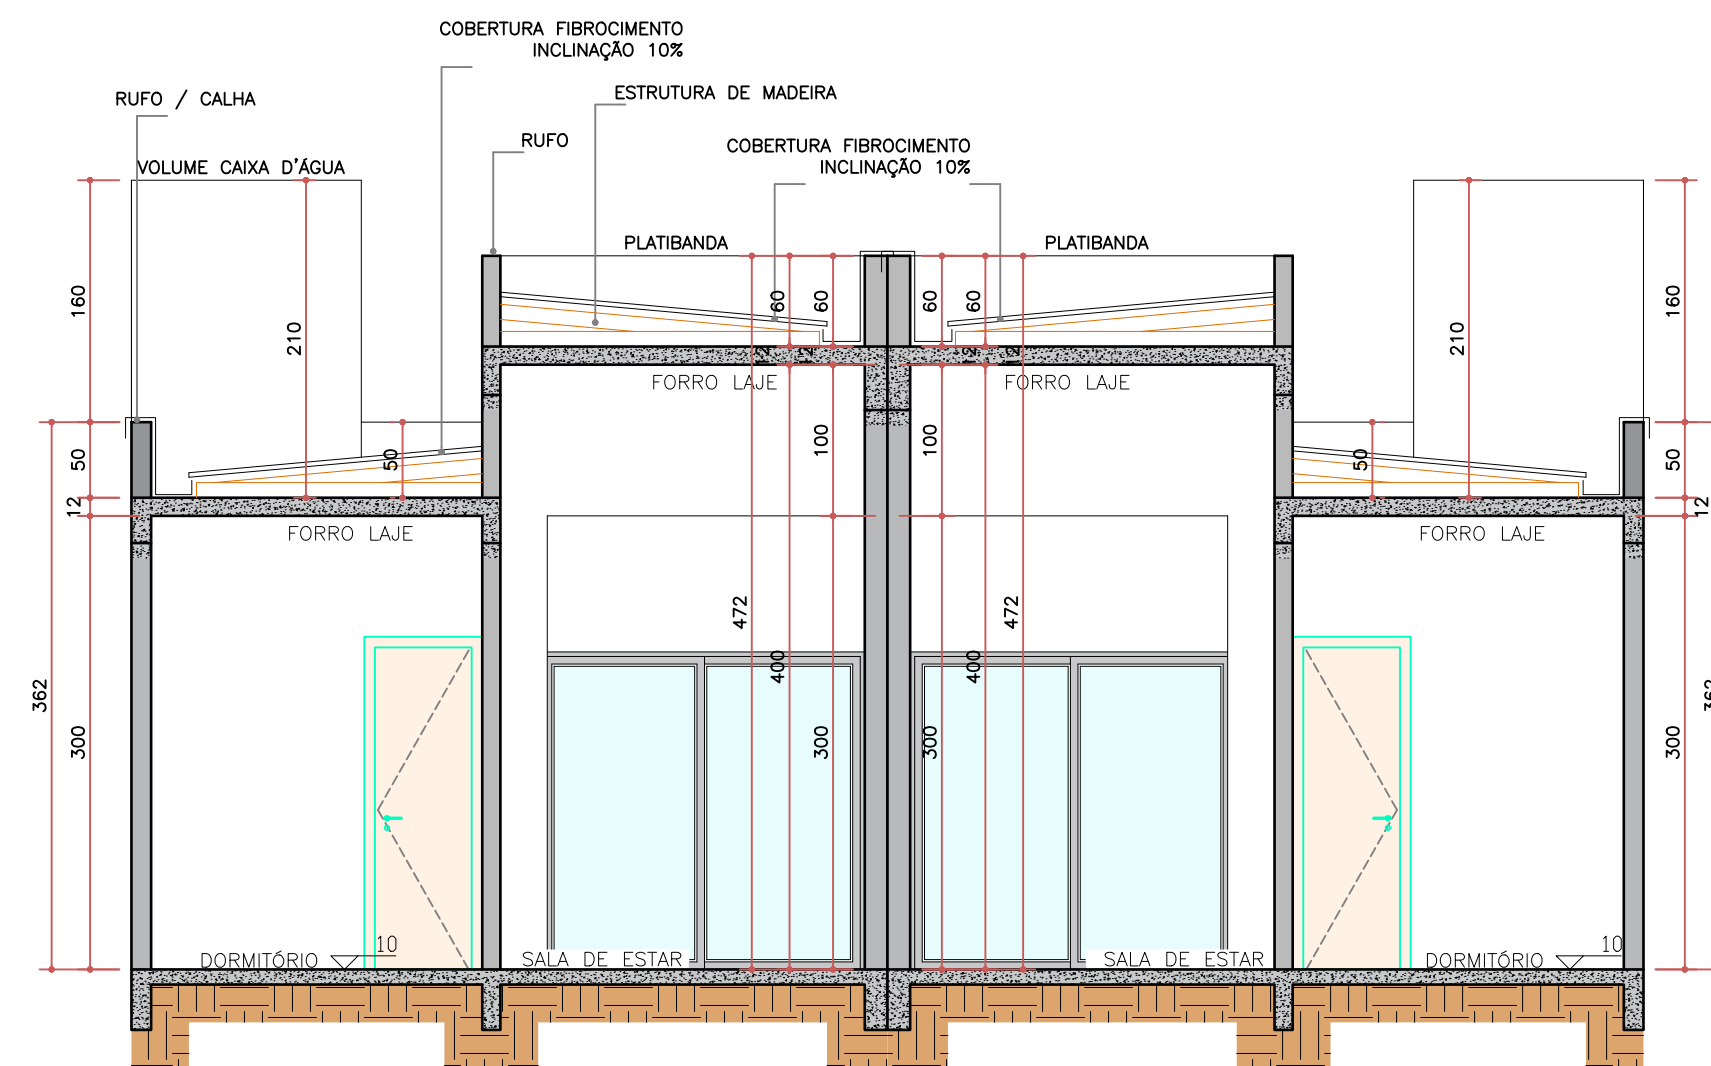

CORTE A1
ESCALA: 1/50

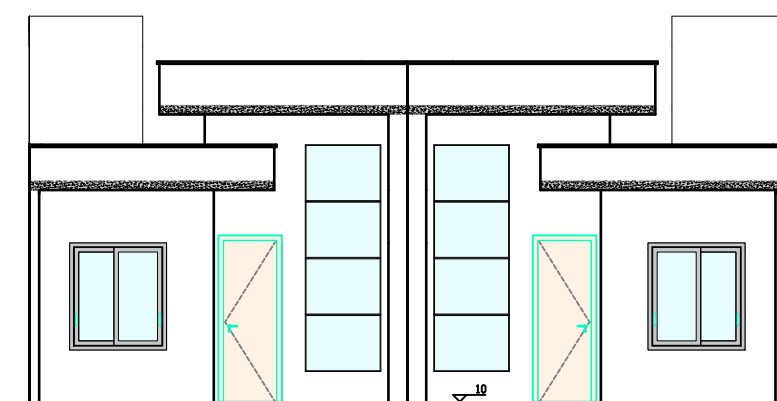

ELEVACÃO
ESCALA: 1:100

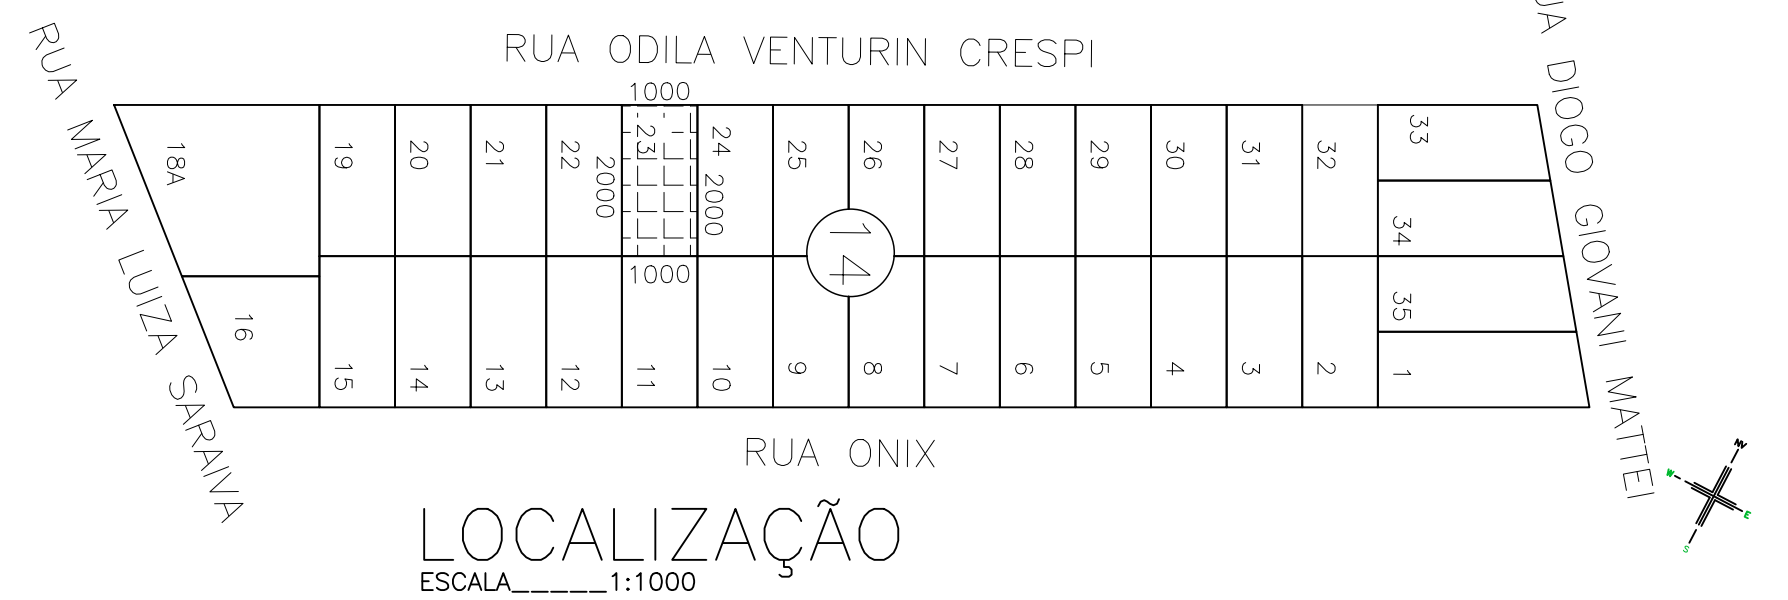

LOCALIZAÇÃO
ESCALA: 1:1000

- NOTAS
- COTAS EM CENTÍMETROS;
 - COTAS DE NÍVEL EM METROS;
 - CONFERIR MEDIDAS, NÍVEIS E PRUMOS NO LOCAL;
 - MEDIDAS EM COTAS PREVALECEM SOBRE O DESENHO;
 - ESSE DESENHO DEVE SER IMPRESSO COLORIDO;

DATA	DESENHO	RESPONSÁVEL	FOLHA
16/06/2025	MAYCON ALMEIDA	MAYCON ALMEIDA	01
ESCALA	ARQUIVO	DISCIPLINA	FASE
ESCALA	2026.05.05.DWG	ARQUITETONICO EXECUTIVO	01
COD. DO PROJETO	0025		

LOCALIZAÇÃO	QUADRO DE ÁREAS (DINÂMICO)
	Área Terreno: 200 m²
	UNIDADE 01
	A. Const.: 60.00 m²
	» TOTAL UNIDADE 01: 60.00 m²
	UNIDADE 02
	A. Const.: 60.00 m²
	» TOTAL UNIDADE 02: 60.00 m²
	» TOTAL UNIDADE 03: 60.00 m²
	DETALHAMENTO DE ÁREAS EXTERNAS
	- Área Total Piso Cerâmico: 14.32 m²
	- Área Total Muros: 4.08 m²
	RESUMO DO EMPREENDIMENTO
	Área Total Construída: 120.00 m²
	Área de Construção Computável: 120.00 m²
	Área Total Impermeável: 138.40 m²
	Área Total permeável: 61.60 m²
	Taxa de Oupação (T.O.): 60.00%
	Coef. Aproveitamento (C.A.): 0.60
	Taxa de Permeabilidade (T.P.): 30.80%

TÍTULO: PLANTA BAIXA
PLANTA COBERTURA
PLANTA SITUAÇÃO
PLANTA LOCALIZAÇÃO
ELEVACÃO E CORTES

TRABALHO DESENVOLVIDO POR:

Projeto Arquitetônico
Maycon Felipe de Almeida
CAU PR: 170768-4

Execução de Obra
Maycon Felipe de Almeida
CAU PR: 170768-4

PROPRIETÁRIO
Carlos Andre Marques Schulze
CPF: 752.405.649-49